

GROUND FLOOR ALPHA-2

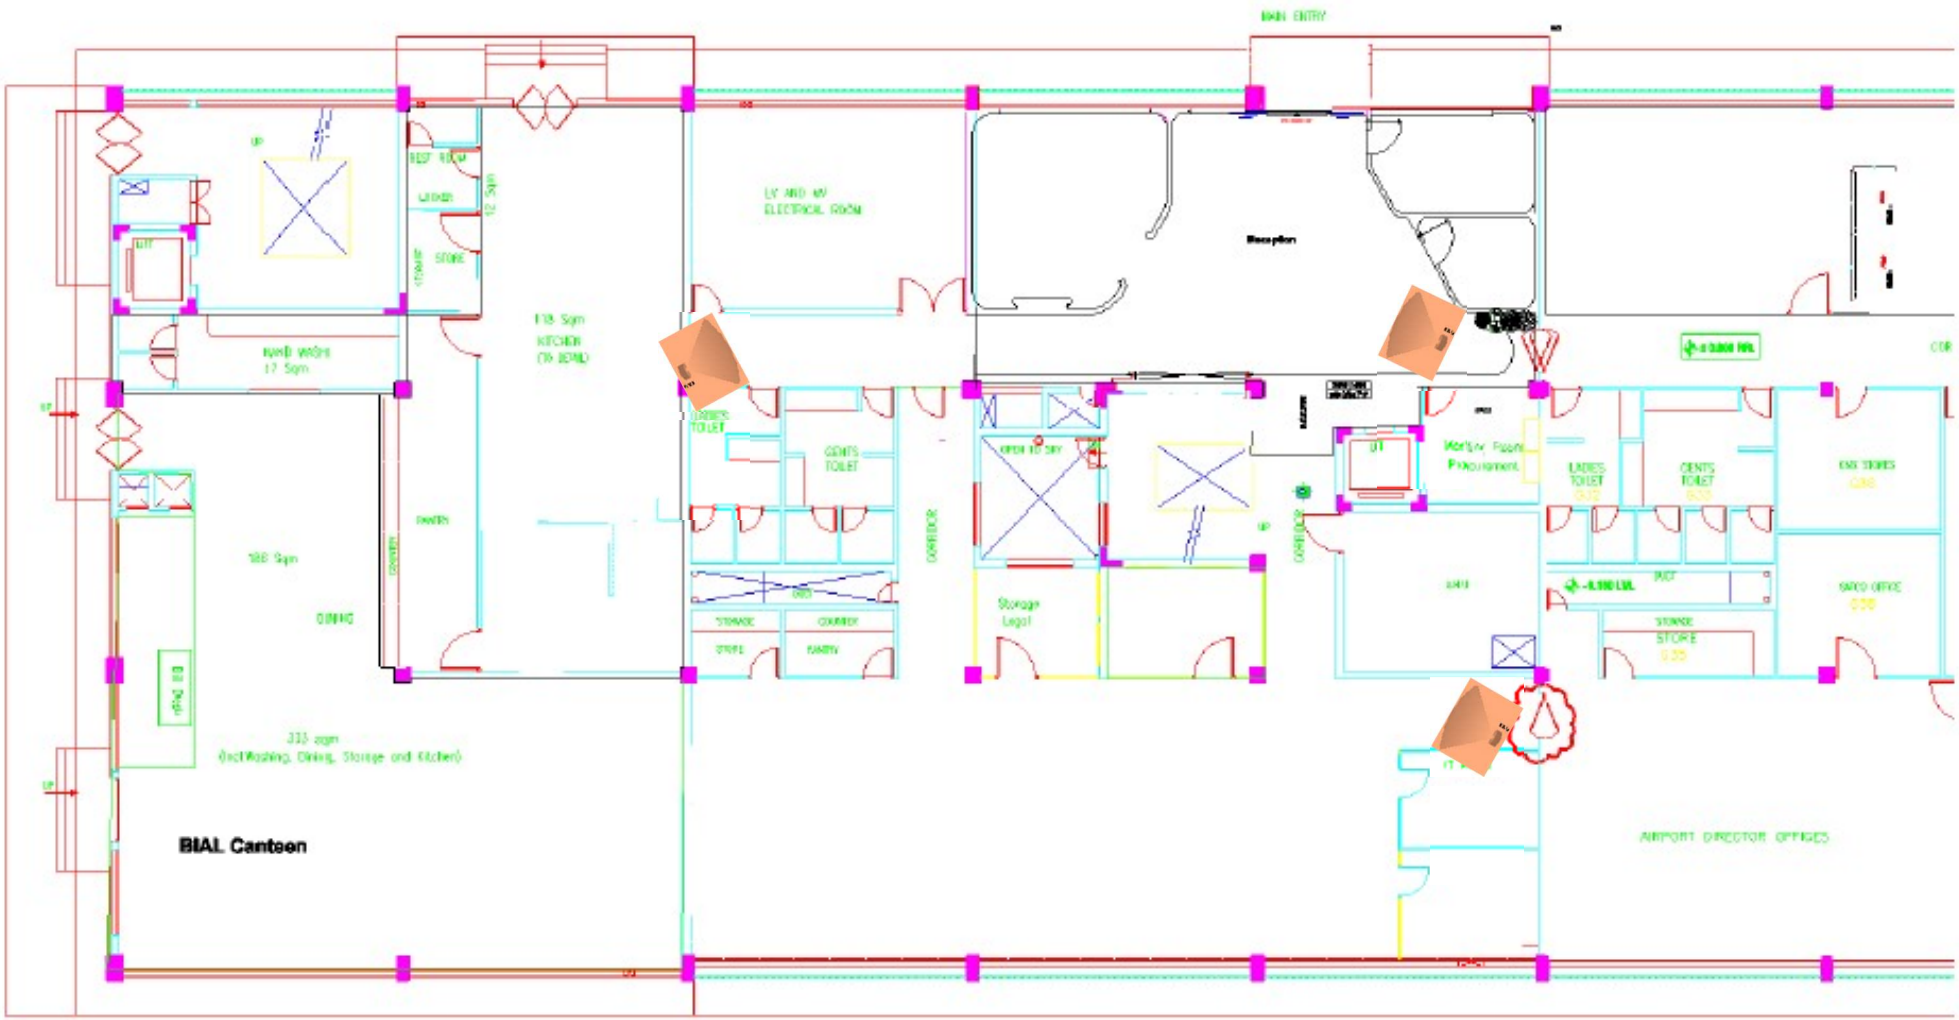


CMS MAINTENANCE ROOM
LADIES REST ROOM
LOCKER ROOM
CMS EXECUTIVES ROOM
GENTS REST ROOM
CMS ROOM
TECHNICAL SUPERVISOR
REST ROOM
REST ROOM LADIES
REST ROOM GENTS
STORE
PANTRY
RADIATING ADS/ OTHER EXT INTERFACE ROOM
LIFT
LADIES TOILET
GENTS TOILET
AUTOMATION SERVER ROOM (MAIN)
CYBER SECURITY AND ASMCCS T&E ROOM
DISTRIBUTION PANEL 2
DISTRIBUTION PANEL 1
VHF/VCCS/DATO/DATA ROOM
BATTERY ROOM
Precision ACs
FALLBACK SERVERS ROOM

ALPHA-2 - FIRST FLOOR

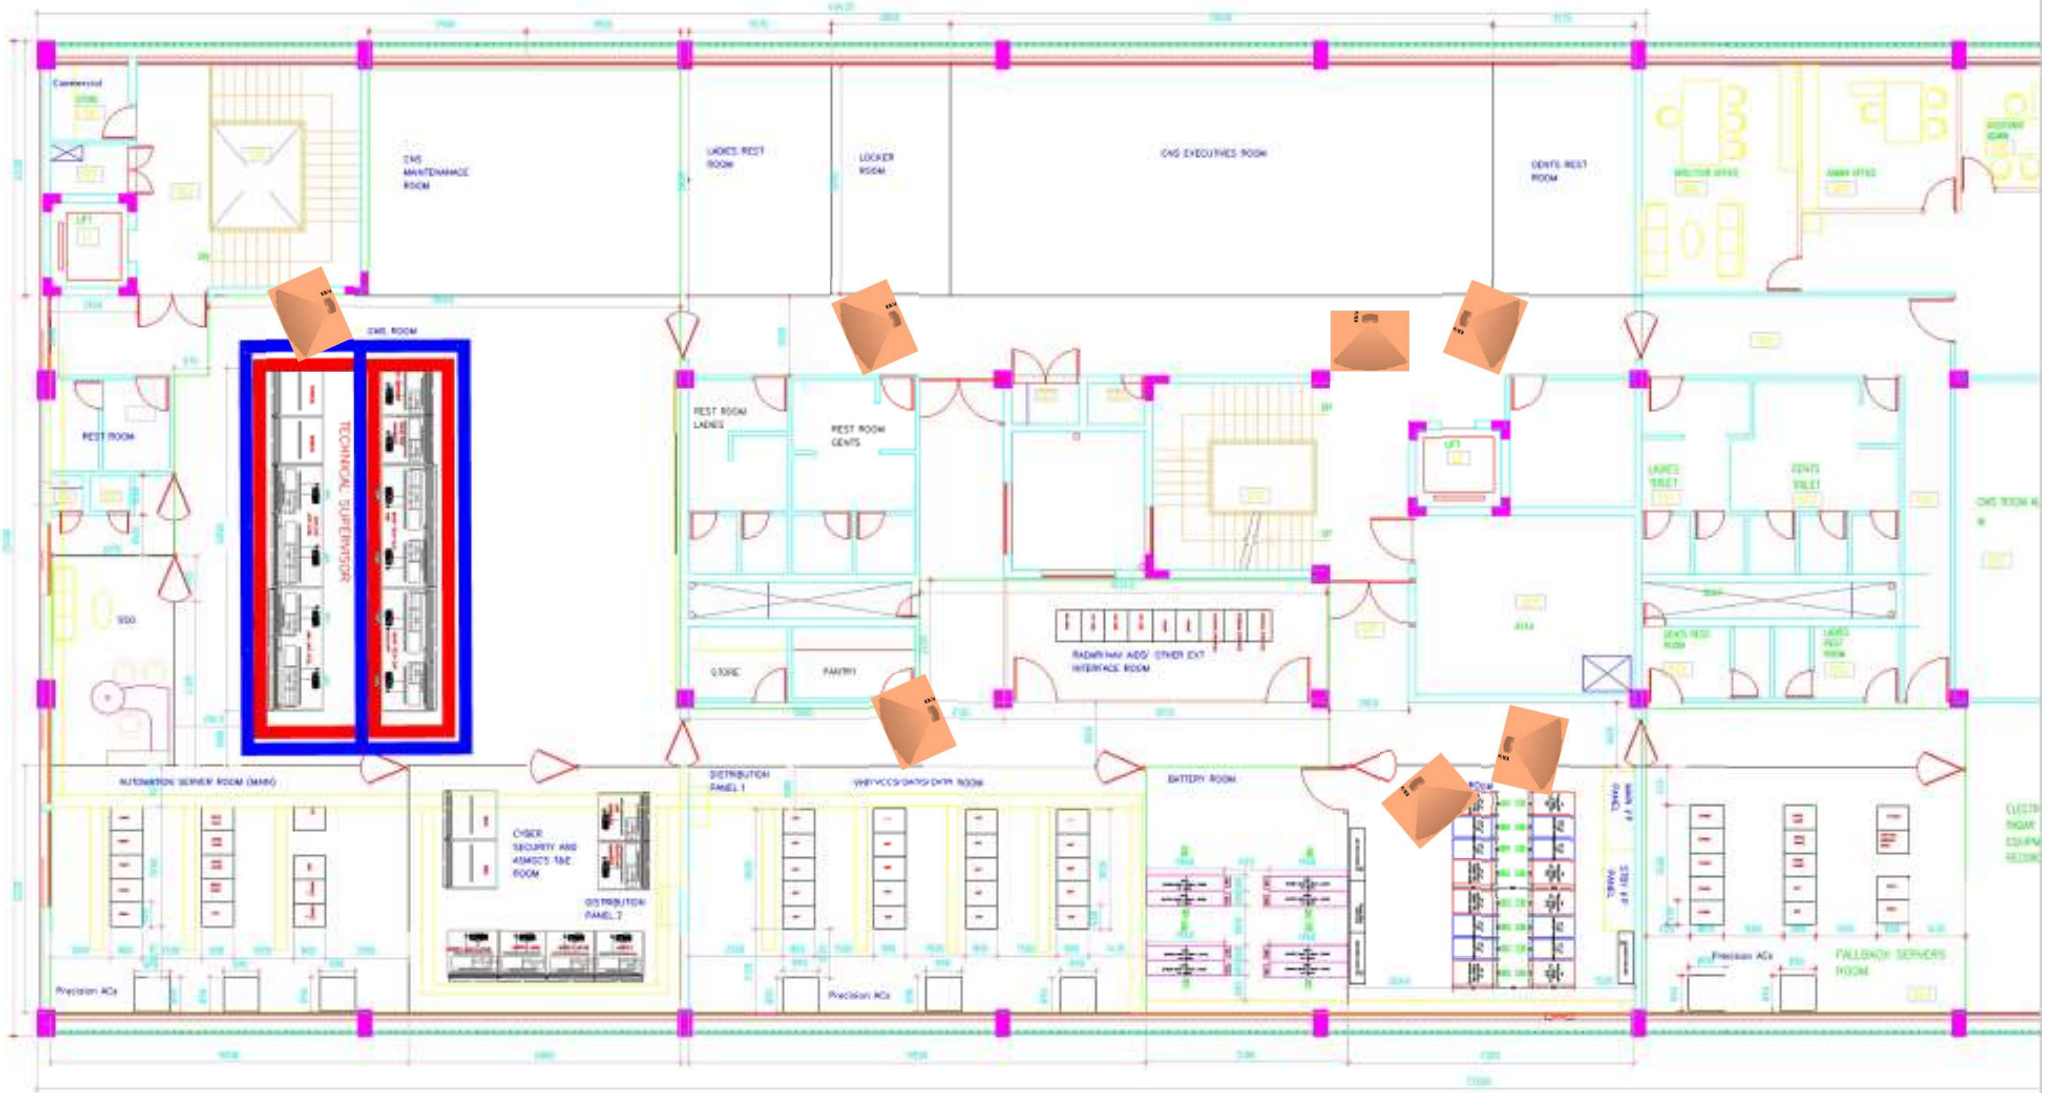